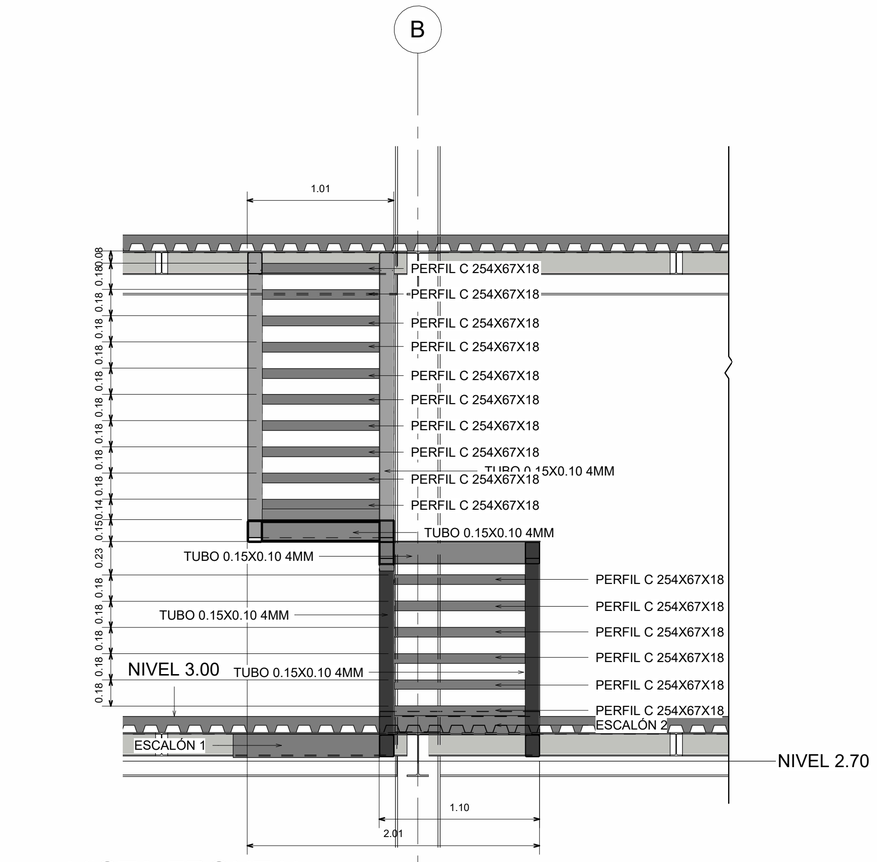
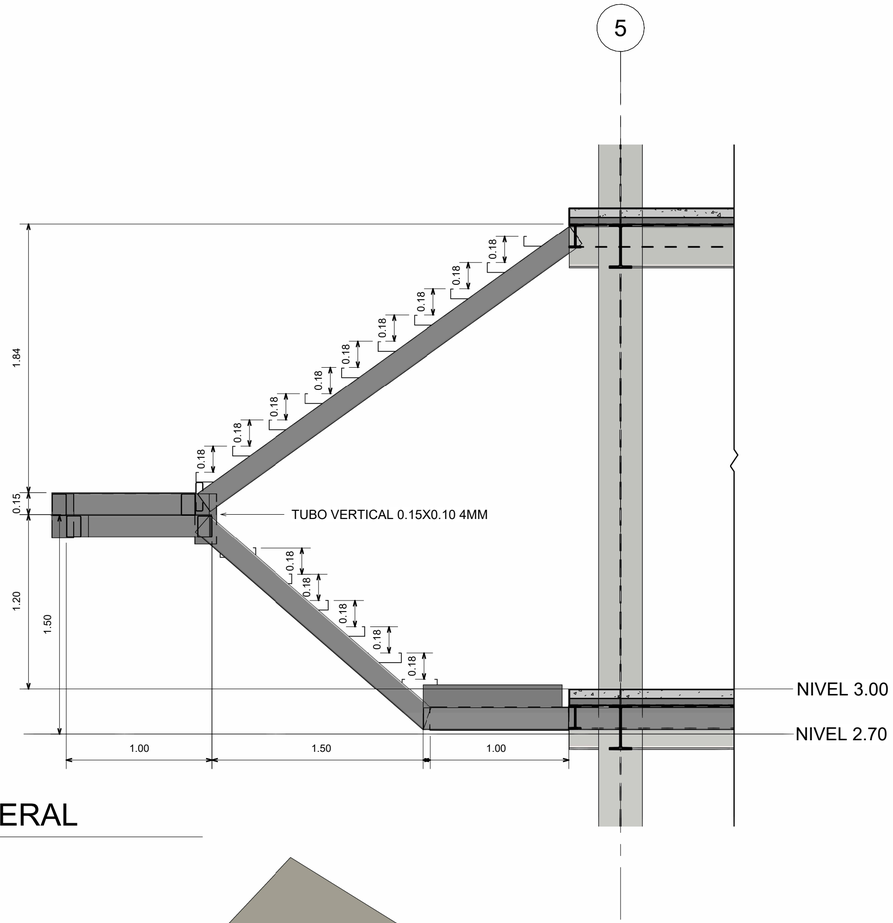
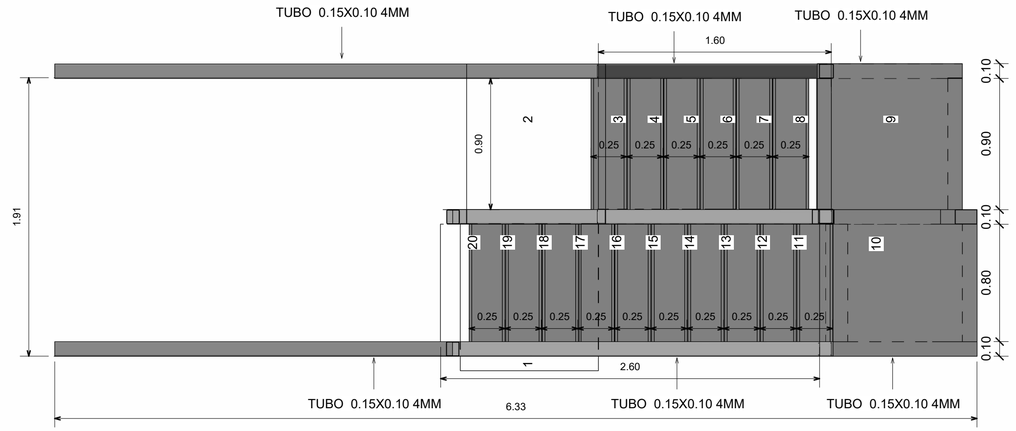


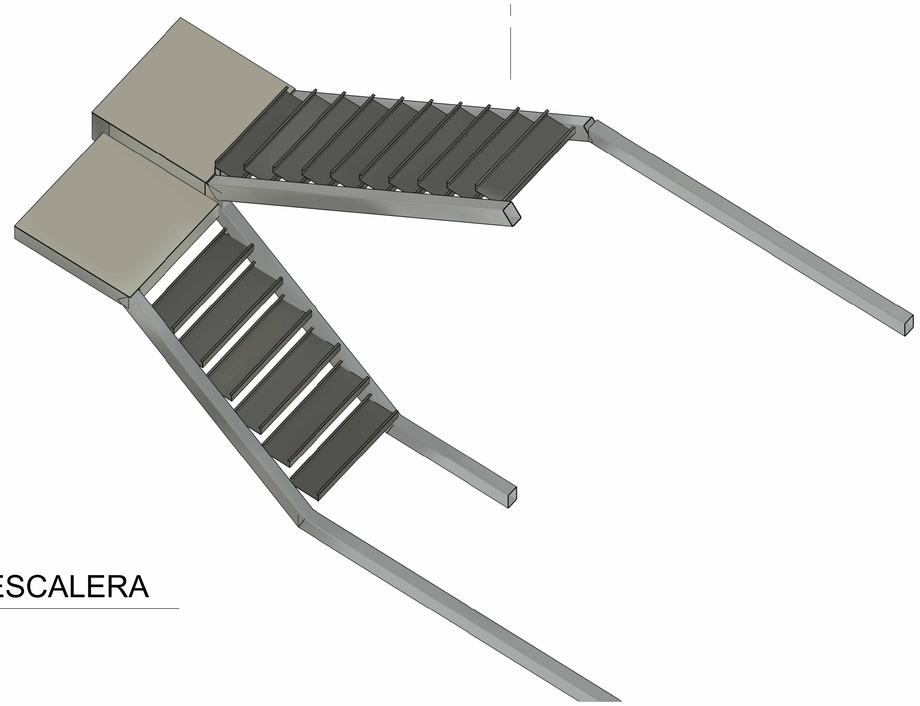

1 VISTA FRONTAL
1 : 25




2 VISTA LATERAL
1 : 25




5 VISTA EN PLANTA
1 : 25



4 VISTA 3D - ESCALERA

| | | | |
|---|---|---|---|
| INGENIA STRUCTURAL CO. | Proyecto: OFICINA 3 NIVELES PARA SEDE ADMINISTRATIVA DOLMEN S.A. | Diseño Arquitectonico: JULIO ALANDETE | |
| | Cliente: DOLMEN S.A | Calculó: ING. OSNAIDER PATERNINA | |
| | Dirección: Enter address here | Revisó: ING. ANDRES GALÁN | |

| PARÁMETROS DE DISEÑO (NORMA NSR-10) | |
|---|---|
| Zona Amenaza sísmica: | baja |
| Perfil de suelo: | D |
| Coeficientes sísmicos | |
| Disipación energía DMI, ro: | = 3.0 |
| Grupo de uso | I |
| Importancia: | I = 1.0 |
| Aceleración piso efectiva: | Aa=0.10 |
| Aceleración piso efectiva: | Av=0.10 |
| Perfil de Suelo: | D |

NOTAS

- Verificar todas las dimensionesen obra antes de trazar.
- los niveles indicados corresponden a cotas de tope de zapata, zarpas y/o vigas de amarre.
- Las zapatas y las vigas de enlace se deben fundir al mismo tiempo.

CARGAS SOBRE IMPUESTAS

Carga Muerta Sobreimpuesta :
Oficina: 2.20 KPa
Cerramiento: 6.0 kN/m
Carga Viva :
Oficina: 2.0 KPa
Escalera: 3.0 KPa
Tanques: 2.0 KPa A N + 11.35
Ganchos: 90 kN A N + 11.35
Ascensor:
Peso: 18 kN A N + 9.60

| MATERIALES | |
|---|---|
| Cimentacion f'c : | 24.5 MPa |
| Acero de Refuerzo f'y: | 420 MPa |
| Platinas: | ASTM A572-50 |
| Columnas, Vigas: | ASTM A 992-50 |
| Barras roscadas: | ASTM A 193-17 GR B7 |

Contiene:
DETALLES DE ESCALERA

| | | | |
|---|---|---|---|
| Número de Proyecto | 160 | E-07 | |
| Fecha | 18/12/2023 | | |
| Dibujó | Autor | | |
| Verificó | Autorizador | Escala | 1 : 25 |

16/1/2024 17:12:27